MAP SHOWING BOUNDARY, SURVEY OF A PORTION OF LOTS 9 & 11 BLOCK 26 AS SHOWN ON MAP OF ORTEGA FARMS

AS RECORDED IN PLAT BOOK 3 PAGE 79 OF THE CURRENT PUBLIC RECORDS OF DUVAL COUNTY, FLORIDA,
AND BEING MORE PARTICULARLY DESCRIBED AS FOLLOWS;

(SURVEYORS DESCRIPTION)

*FOR A **POINT OF REFERENCE**, COMMENCE AT THE SOUTHEAST CORNER OF LOT 15, AS SHOWN ON MAP OF TIMUQUANA HEIGHTS REPLAT, AS RECORDED IN PLAT BOOK 33, PAGE 67 OF THE CURRENT PUBLIC RECORDS OF DUVAL COUNTY, FLORIDA, WITH THE EASTERLY LINE OF LOT 11, BLOCK 26, AS SHOWN ON THE MAP OF ORTEGA FARMS, RECORDED IN PLAT BOOK 3, PAGE 79, OF THE CURRENT PUBLIC RECORDS OF DUVAL COUNTY, FLORIDA: THENCE NORTH 89°56'41" EAST ALONG THE SOUTHERLY LINE OF THOSE LANDS DESCRIBED IN OFFICIAL RECORDS BOOK 16991, PAGE 1706, AND OFFICIAL RECORDS BOOK 16671, PAGE 1576, BOTH AFOREMENTIONED BEING RECORDED IN THE CURRENT PUBLIC RECORDS OF SAID COUNTY, A DISTANCE OF 324.81 FEET TO THE WESTERLY LINE OF THOSE LANDS DESCRIBED IN OFFICIAL RECORDS BOOK 18985, PAGE 692 OF THE CURRENT PUBLIC RECORDS OF SAID COUNTY AND TO THE **POINT OF BEGINNING**; THENCE SOUTH 00°05'08" EAST ALONG THE THOSE LAST AFOREMENTIONED LANDS, A DISTANCE OF 511.01 FEET TO THE NORTHERLY RIGHT OF WAY LINE OF 103RD STREET (STATE ROAD 104, A 104 FOOT RIGHT OF WAY AS PRESENTLY ESTABLISHED, AN 80 FOOT RIGHT OF WAY AS FORMERLY ESTABLISHED) THENCE SOUTH 89°29'49" WEST ALONG THE NORTH LINE OF THE LAST AFOREMENTIONED RIGHT OF WAY LINE, A DISTANCE OF 509.25 FEET; THE FOLLOWING (5) COURSES WILL RUN ALONG THE EAST LINE OF THOSE LANDS DESCRIBED IN OFFICIAL RECORDS BOOK 17745, PAGE 1252, OF SAID COUNTY*

*THENCE DEPARTING SAID RIGHT OF WAY LINE, NORTH 00°23'21" EAST, A DISTANCE OF 117.07 FEET: SOUTH 88°01'41" WEST, A DISTANCE OF 19.33 FEET; THENCE NORTH 00°05'06" WEST A DISTANCE OF 101.00 FEET; THENCE NORTH 88°08'59" WEST, A DISTANCE OF 1.50 FEET; THENCE NORTH 00°14'05" WEST, A DISTANCE OF 5.00 FEET; THENCE SOUTH 87°44'26" WEST ALONG THE NORTH LINE OF THOSE LANDS DESCRIBED IN OFFICIAL RECORDS BOOK 17745, PAGE 1252, OF SAID COUNTY, A DISTANCE OF 112.67 FEET TO A POINT OF INTERSECTION; THENCE NORTH 89°56'30" WEST ALONG THE NORTH LINE OF THOSE LANDS DESCRIBED IN OFFICIAL RECORDS BOOK 19998, PAGE 167, OF THE PUBLIC RECORDS OF SAID COUNTY, A DISTANCE OF 75.83 FEET TO THE EASTERLY LINE OF THE AFOREMENTIONED LANDS; THENCE NORTH 00°05'06" WEST ALONG THE EASTERLY LINE OF THE AFOREMENTIONED LANDS, A DISTANCE OF 296.77 FEET TO THE SOUTHERLY LINE OF A 10 FOOT DRAINAGE RIGHT OF WAY, AS SHOWN ON MAP OF TIMUQUANA HEIGHTS REPLAT, AS RECORDED IN PLAT BOOK 33, PAGE 67 OF THE CURRENT RECORDS OF SAID COUNTY; THENCE NORTH 89°56'41" EAST ALONG THE SOUTH LINE OF THE AFOREMENTIONED PLAT, A DISTANCE OF 717.39 FEET TO THE **POINT OF BEGINNING;***

LESS AND EXCEPT THAT PORTION RECORDED IN OFFICIAL RECORDS BOOK 13695 PAGE 384 AS TO EXHIBIT A IN SAID SPECIAL WARRANTY DEED

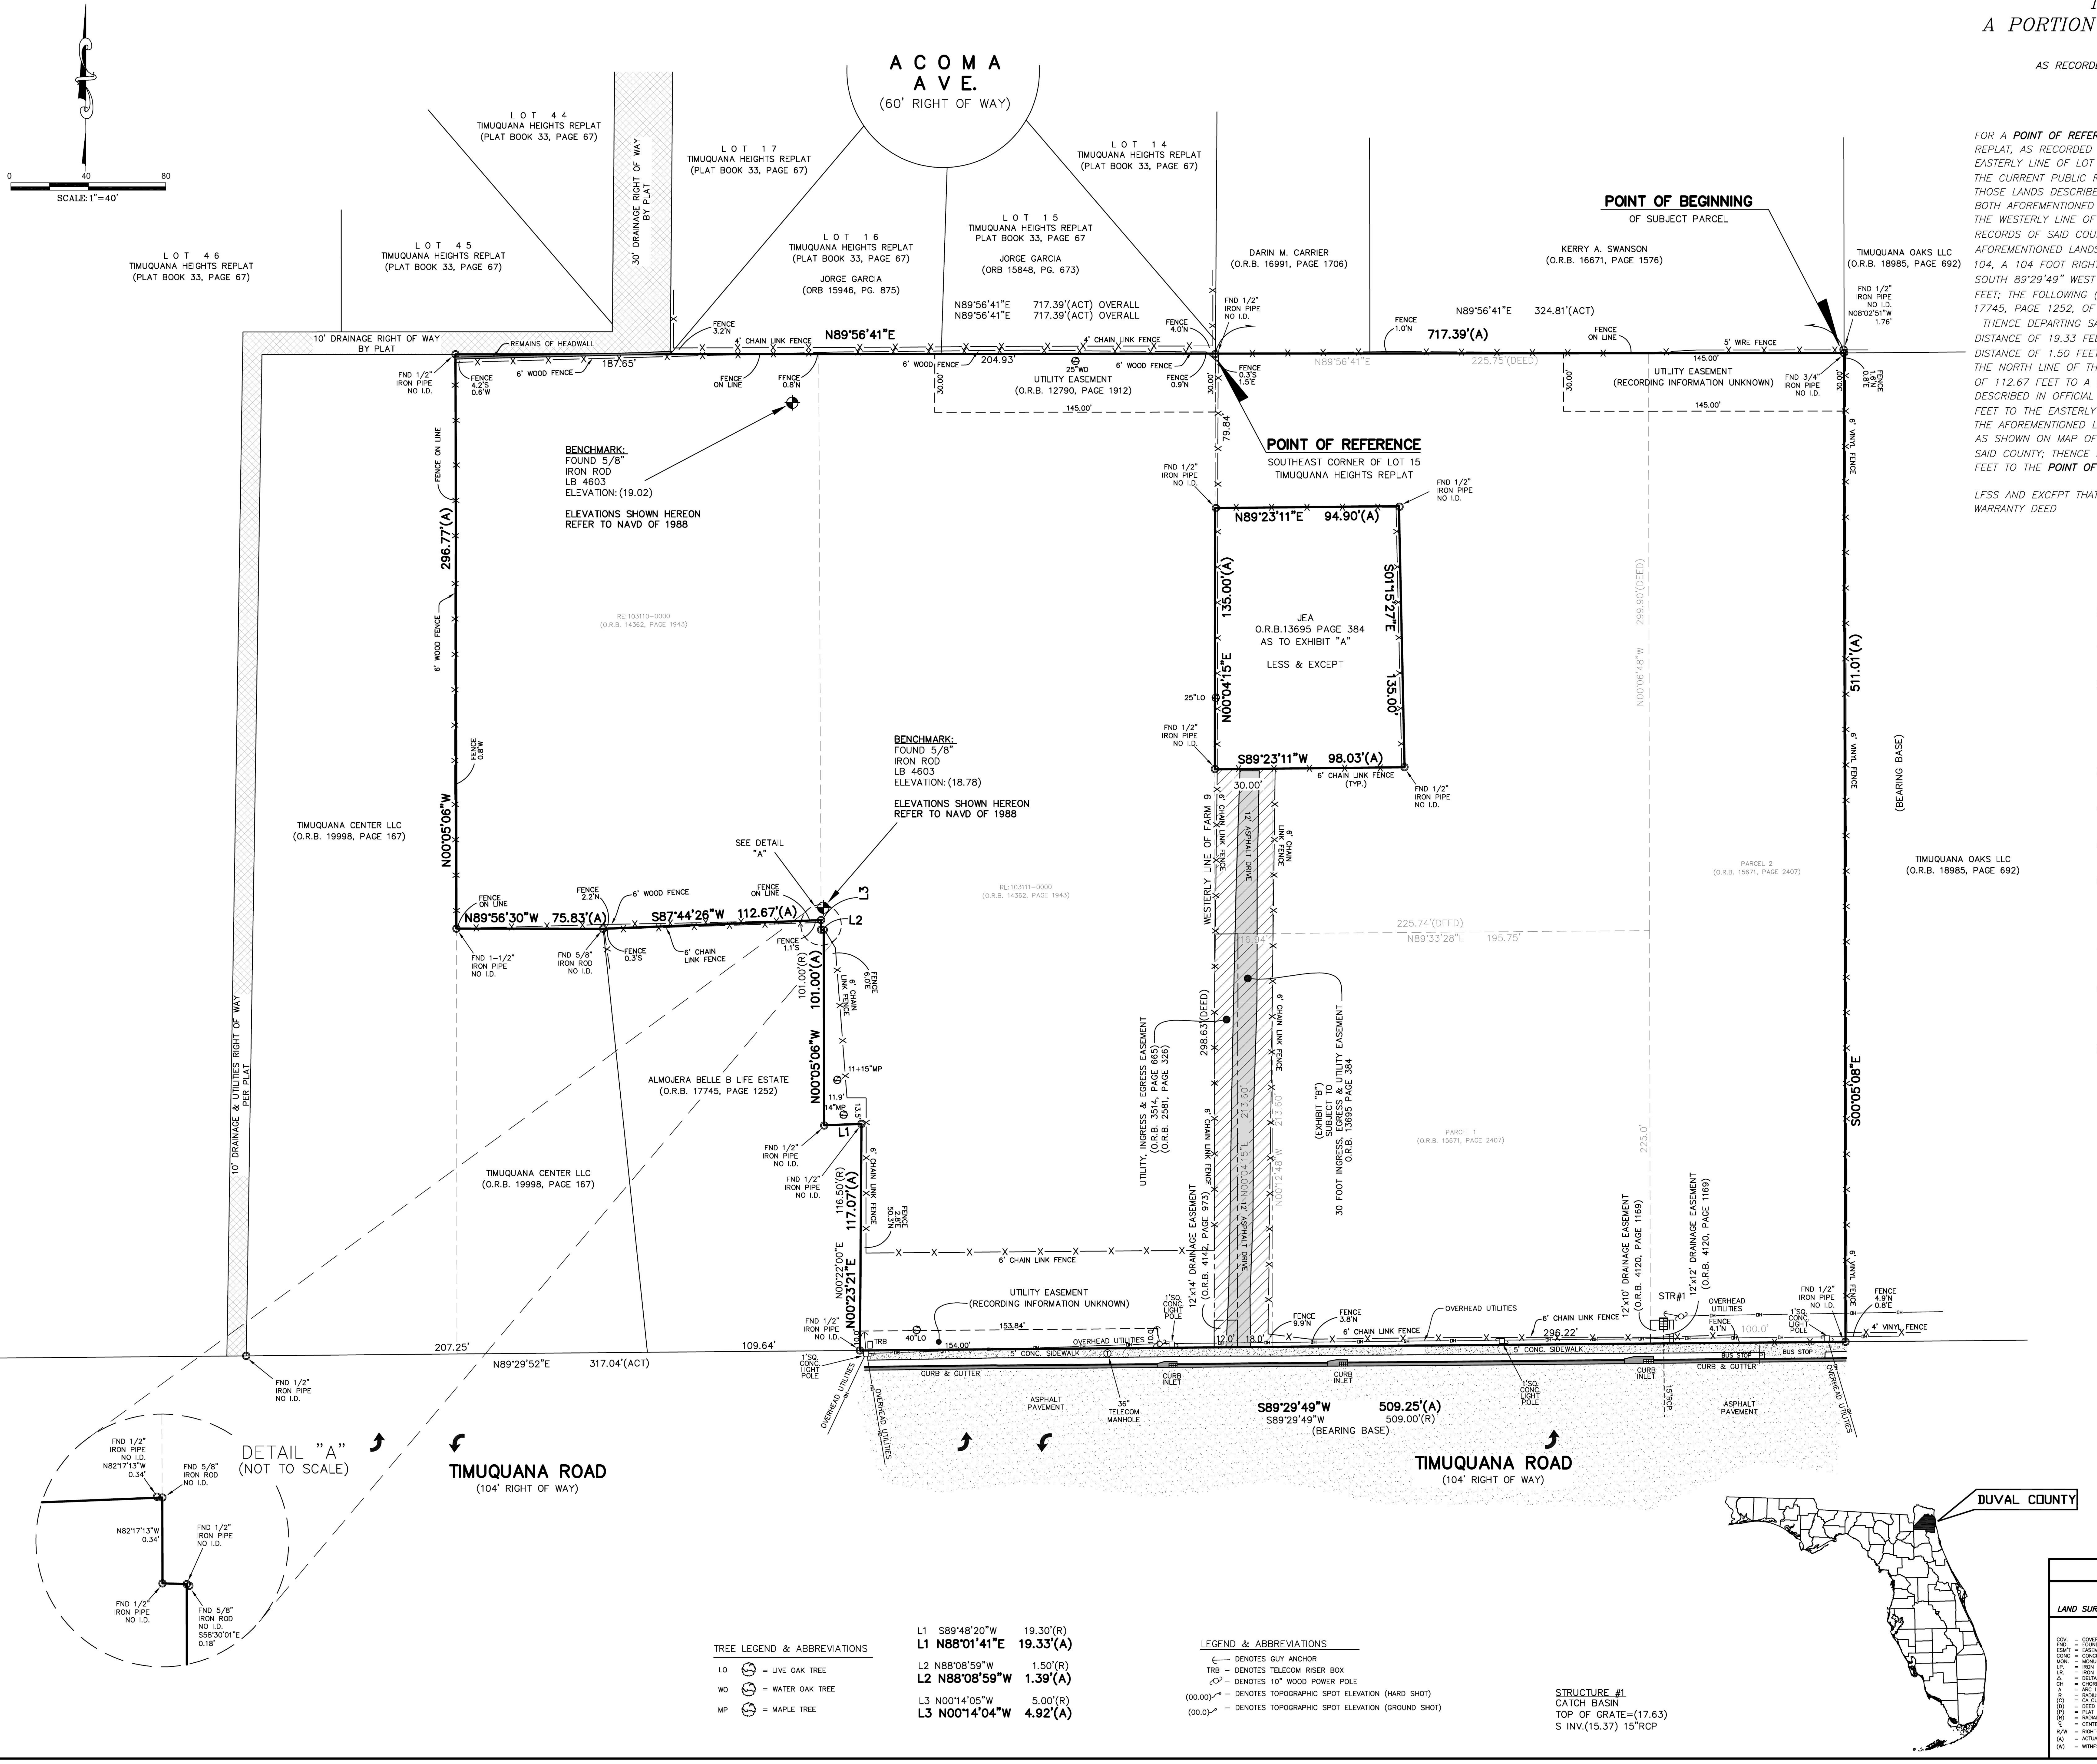
0
40
80
SCALE: 1"=40'
ACOMA AVE.
(60' RIGHT OF WAY)
LOT 44 TIMUQUANA HEIGHTS REPLAT (PLAT BOOK 33, PAGE 67)
LOT 45 TIMUQUANA HEIGHTS REPLAT (PLAT BOOK 33, PAGE 67)
LOT 46 TIMUQUANA HEIGHTS REPLAT (PLAT BOOK 33, PAGE 67)
LOT 17 TIMUQUANA HEIGHTS REPLAT (PLAT BOOK 33, PAGE 67)
LOT 16 TIMUQUANA HEIGHTS REPLAT (PLAT BOOK 33, PAGE 67)
JORGE GARCIA (ORB 15946, PG. 875)
LOT 15 TIMUQUANA HEIGHTS REPLAT PLAT BOOK 33, PAGE 67
JORGE GARCIA (ORB 15848, PG. 673)
LOT 14 TIMUQUANA HEIGHTS REPLAT (PLAT BOOK 33, PAGE 67)
30' DRAINAGE RIGHT OF WAY BY PLAT
10' DRAINAGE RIGHT OF WAY BY PLAT
REMAINS OF HEADWALL
N89°56'41"E 717.39'(ACT) OVERALL
N89°56'41"E 717.39'(ACT) OVERALL
N89°56'41"E
187.65'
204.93'
4' CHAIN LINK FENCE
6' WOOD FENCE
25"WO
UTILITY EASEMENT (O.R.B. 12790, PAGE 1912)
145.00'
30.00'
DARIN M. CARRIER (O.R.B. 16991, PAGE 1706)
KERRY A. SWANSON (O.R.B. 16671, PAGE 1576)
N89°56'41"E 324.81'(ACT)
717.39'(A)
225.75'(DEED)
5' WIRE FENCE
UTILITY EASEMENT (RECORDING INFORMATION UNKNOWN)
POINT OF BEGINNING
OF SUBJECT PARCEL
TIMUQUANA OAKS LLC (O.R.B. 18985, PAGE 692)
FND 1/2" IRON PIPE NO I.D. N08°02'51"W 1.76'
FND 3/4" IRON PIPE NO I.D.
POINT OF REFERENCE
SOUTHEAST CORNER OF LOT 15 TIMUQUANA HEIGHTS REPLAT
79.84'
FND 1/2" IRON PIPE NO I.D.
N89°23'11"E 94.90'(A)
135.00'(A)
S01°15'27"E
N00°04'15"E
135.00'
JEA O.R.B.13695 PAGE 384 AS TO EXHIBIT "A"
LESS & EXCEPT
25"LO
S89°23'11"W 98.03'(A)
6' CHAIN LINK FENCE (TYP.)
30.00'
BENCHMARK: FOUND 5/8" IRON ROD LB 4603 ELEVATION: (19.02)
ELEVATIONS SHOWN HEREON REFER TO NAVD OF 1988
BENCHMARK: FOUND 5/8" IRON ROD LB 4603 ELEVATION: (18.78)
ELEVATIONS SHOWN HEREON REFER TO NAVD OF 1988
RE:103110-0000 (O.R.B. 14362, PAGE 1943)
RE:103111-0000 (O.R.B. 14362, PAGE 1943)
296.77'(A)
N00°05'06"W
TIMUQUANA CENTER LLC (O.R.B. 19998, PAGE 167)
SEE DETAIL "A"
L1
L2
L3
N89°56'30"W 75.83'(A)
S87°44'26"W 112.67'(A)
FND 1-1/2" IRON PIPE NO I.D.
FND 5/8" IRON ROD NO I.D.
101.00'(R)
101.00'(A)
N00°05'06"W
11+15"MP
14"MP
ALMOJERA BELLE B LIFE ESTATE (O.R.B. 17745, PAGE 1252)
116.50'(R)
117.07'(A)
N00°22'00"E
N00°23'21"E
10' DRAINAGE & UTILITIES RIGHT OF WAY PER PLAT
TIMUQUANA CENTER LLC (O.R.B. 19998, PAGE 167)
207.25'
109.64'
N89°29'52"E 317.04'(ACT)
WESTERLY LINE OF FARM 9
12' ASPHALT DRIVE
225.74'(DEED)
N89°33'28"E 195.75'
298.63'(DEED)
213.60'
UTILITY, INGRESS & EGRESS EASEMENT (O.R.B. 3514, PAGE 665) (O.R.B. 2581, PAGE 326)
(EXHIBIT "B") SUBJECT TO 30 FOOT INGRESS, EGRESS & UTILITY EASEMENT O.R.B. 13695 PAGE 384
12'x14' DRAINAGE EASEMENT (O.R.B. 4142, PAGE 973)
PARCEL 2 (O.R.B. 15671, PAGE 2407)
PARCEL 1 (O.R.B. 15671, PAGE 2407)
N00°06'48"W 299.90'(DEED)
225.0'
511.01'(A)
S00°05'08"E
(BEARING BASE)
TIMUQUANA OAKS LLC (O.R.B. 18985, PAGE 692)
6' VINYL FENCE
12'x10' DRAINAGE EASEMENT (O.R.B. 4120, PAGE 1169)
12'x12' DRAINAGE EASEMENT (O.R.B. 4120, PAGE 1169)
STR#1
296.22'
100.0'
OVERHEAD UTILITIES
5' CONC. SIDEWALK
CURB & GUTTER
CURB INLET
BUS STOP
1'SQ. CONC. LIGHT POLE
36" TELECOM MANHOLE
ASPHALT PAVEMENT
40"LO
153.84'
154.00'
TRB
S89°29'49"W 509.25'(A)
S89°29'49"W 509.00'(R)
(BEARING BASE)
TIMUQUANA ROAD
(104' RIGHT OF WAY)
DETAIL "A"
(NOT TO SCALE)
FND 1/2" IRON PIPE NO I.D. N82°17'13"W 0.34'
FND 5/8" IRON ROD NO I.D.
N82°17'13"W 0.34'
FND 1/2" IRON PIPE NO I.D.
FND 5/8" IRON ROD NO I.D. S58°30'01"E 0.18'
DUVAL COUNTY

TREE LEGEND & ABBREVIATIONS

LO = LIVE OAK TREE
WO = WATER OAK TREE
MP = MAPLE TREE

L1	S89°48'20"W	19.30'(R)
L1	**N88°01'41"E**	**19.33'(A)**
L2	N88°08'59"W	1.50'(R)
L2	**N88°08'59"W**	**1.39'(A)**
L3	N00°14'05"W	5.00'(R)
L3	**N00°14'04"W**	**4.92'(A)**

LEGEND & ABBREVIATIONS

← DENOTES GUY ANCHOR
TRB – DENOTES TELECOM RISER BOX
DENOTES 10" WOOD POWER POLE
(00.00) – DENOTES TOPOGRAPHIC SPOT ELEVATION (HARD SHOT)
(00.0) – DENOTES TOPOGRAPHIC SPOT ELEVATION (GROUND SHOT)

STRUCTURE #1
CATCH BASIN
TOP OF GRATE=(17.63)
S INV.(15.37) 15"RCP

GENERAL SURVEY NOTES:

1. THIS SURVEY WAS MADE IN ACCORDANCE WITH LAWS AND/OR STANDARDS OF PRACTICE OF THE STATE OF FLORIDA.
2. THE BASIS OF BEARING FOR THIS SURVEY IS BASED ON THE WESTERLY LINE OF THOSE LANDS DESCRIBED IN OFFICIAL RECORDS BOOK 18985, PAGE 692 OF THE CURRENT PUBLIC RECORDS OF DUVAL COUNTY, FLORIDA, AND THE NORTHERLY RIGHT OF WAY LINE OF STATE ROAD 104, AKA TIMUQUANA ROAD (A 104 FOOT FOOT RIGHT OF WAY AS PRESENTLY ESTABLISHED
3. THE PROPERTY HAS DIRECT ACCESS TO TIMUQUANA ROAD, A DEDICATED PUBLIC STREET OR HIGHWAY.
4. THERE IS NO OBSERVED EVIDENCE OF CURRENT EARTH MOVING WORK, BUILDING CONSTRUCTION OR BUILDING ADDITIONS.
5. THIS SURVEY WAS PERFORMED WITHOUT THE BENEFIT OF A TITLE COMMITMENT. ALL EASEMENTS NOTED IN TITLE SEARCH PROVIDED TO US ARE INCLUDED IN THIS SURVEY
6. THIS SURVEY WAS PRODUCED AND BASED ON FIELD MONUMENTATION, OCCUPATION AND AVAILABLE RECORDS THROUGH LOCAL AND STATE MUNICIPALITIES WHERE AVAILABLE. SURVEY WAS MADE TO THE BEST OF OUR ABILITY AND THROUGH THE USE OF BEST PRACTICES. PLATS AND OR DEEDS OF RECORD MAY BE VAGUE OR AMBIGUOUS IN NATURE
7. UNDERGROUND ENCROACHMENTS NOT LOCATED. ONLY UTILITIES WITH ABOVE GROUND FEATURES MARKING BELOWGROUND FEATURES WERE LOCATED BY THIS SURVEY.
8. BENCHMARKS SHOWN HERON ARE BASED OFF GPS OBSERVATION OF 600 EPOCHS USING THE L-NET NETWORK. FLORIDA STATE PLANE COORDINATE EAST, NAD 83, NO_TRANS NAVD 1988
9. NO APPARENT WETLANDS ARE LOCATED ON THE SUBJECT PROPERTY ACCORDING TO THE U.S. FISH AND WILDLIFE SERVICE NATIONAL WETLANDS INVENTORY LOCATED AT WWW.FWS.GOV/WETLANDS .

ADDITIONAL NOTES

1. ORDER OF TAKING RECORDED IN OFFICIAL RECORDS BOOK 4144, PAGE 821.RIGHT OF WAY TAKING TO EXPAND TIMUQUANA ROAD FROM AN 80 FOOT RIGHT OF WAY TO A 104 FOOT RIGHT OF WAY
2. DRAINAGE EASEMENT RECORDED IN OFFICIAL RECORDS BOOK 4142, PAGE 973.
3. EASEMENT AS SET FORTH AND RESERVED IN SPECIAL WARRANTY DEED RECORDED IN OFFICIAL RECORDS BOOK 13695, PAGE 384.
4. EASEMENT FOR INGRESS, EGRESS AND UTILITIES AS SET FORTH IN OFFICIAL RECORDS BOOK 3514, PAGE 665.
5. RIGHT OF REVERTER AS CITED IN DEED BOOK 1826, PAGE 333, EXPIRED ON JULY 25TH 1984
6. RIGHT OF REVERTER SET FORTH IN OFFICIAL RECORDS BOOK 2175, PAGE 184 AND OFFICIAL RECORDS BOOK 3158, PAGE 1010.
7. THIRD PARTY BENEFICIARY AGREEMENT RECORDED IN OFFICIAL RECORDS BOOK 2581, PAGE 326.
8. TERMS, PROVISIONS AND OBLIGATIONS AS CONTAINED IN THE WARRANTY DEED IN OFFICIAL RECORDS BOOK 3514, PAGE 665.
9. DRAINAGE EASEMENT RECORDED IN OFFICIAL RECORDS BOOK 4120, PAGE 1169.
10. GRANT OF EASEMENT TO JEA RECORDED IN OFFICIAL RECORDS BOOK 12790, PAGE 1912.
11. EASEMENTS AS SET FORTH AND RESERVED IN SPECIAL WARRANTY DEED RECORDED IN OFFICIAL RECORDS BOOK 13695, PAGE 385.
13. RELEASE OF RESTRICTIVE COVENANT "BLANKET IN NATURE" RECORDED IN OFFICIAL RECORDS BOOK 8474 PAGE 1504

UNDERGROUND ENCROACHMENTS NOT LOCATED

THE LAND SHOWN HEREON IS IN THE SPECIAL FLOOD HAZARD ZONE "X"
AS SHOWN ON FLOOD INSURANCE RATE MAP 0526 J FOR DUVAL COUNTY, FLORIDA, DATED 11-02-18

ALL AMERICAN SURVEYORS OF FLORIDA, INC.
LAND SURVEYORS – 3751 SAN JOSE PLACE, SUITE 15 – JACKSONVILLE, FLORIDA, 32257 – 904/279-0088 – LICENSED LAND BUSINESS NO. 3857

Legend

COV. = COVERED	F.F.E. = FINISH FLOOR ELEVATION
FND. = FOUND	A/C = AIR CONDITIONER
ESM'T = EASEMENT	I.D. = IDENTIFICATION
CONC = CONCRETE	P.R.M. = PERMANENT REFERENCE MONUMENT
MON. = MONUMENT	
I.P. = IRON PIPE	P.T. = POINT OF TANGENCY
I.R. = IRON ROD	P.C.P. = PERMANENT CONTROL POINT
Δ = DELTA ANGLE	P.C. = POINT OF CURVE
CH = CHORD	P.R.C. = POINT OF REVERSE CURVE
A = ARC LENGTH	P.C.C. = POINT OF COMPOUND CURVE
R = RADIUS	B.R.L. = BUILDING RESTRICTION
(C) = CALCULATED	F.P.&L.= FLORIDA POWER & LIGHT
(D) = DEED	(TYP.) = TYPICAL
(P) = PLAT	NGVD = NATIONAL GEODETIC VERTICAL DATUM
(R) = RADIAL LINE	NAVD = NORTH AMERICAN VERTICAL
℄ = CENTER LINE	P.I. = POINT OF INTERSECTION
R/W = RIGHT-OF-WAY	EOW = EDGE OF WATER
(A) = ACTUAL	TOB = TOP OF BANK
(W) = WITNESS	LB = LICENSED BUSINESS

THIS IS TO CERTIFY THAT THE ABOVE LANDS WERE SURVEYED UNDER MY RESPONSIBLE SUPERVISION AND DIRECTION, THAT THERE ARE NO ENCROACHMENTS EXCEPT AS SHOWN AND THAT THE SURVEY SHOWN HEREON MEETS THE STANDARDS OF PRACTICE AS SET FORTH BY THE FLORIDA BOARD OF PROFESSIONAL SURVEYORS AND MAPPERS PURSUANT TO CHAPTER 472.027 / CHAPTER 5J17, FLORIDA ADMINISTRATIVE CODE

SURVEY NOT VALID UNLESS EMBOSSED BY SEAL
JAMES D. HARRISON, JR., No. 2647
MICHAEL A. GARRETT, No. 6643

SCALE 1"=40'

DATE 03-14-2023

James D. Harrison Jr.
FLORIDA REGISTERED SURVEYOR AND MAPPER

ALL AMERICAN SURVEYORS OF FLORIDA, INC.

5
4
9
8

F.B. N/A *D.C.* 92154-217409 *DR. BY* DEL/AJ *DIR.* *ORDER NO.* 217409-EASEMENTS *FILE* 92154